


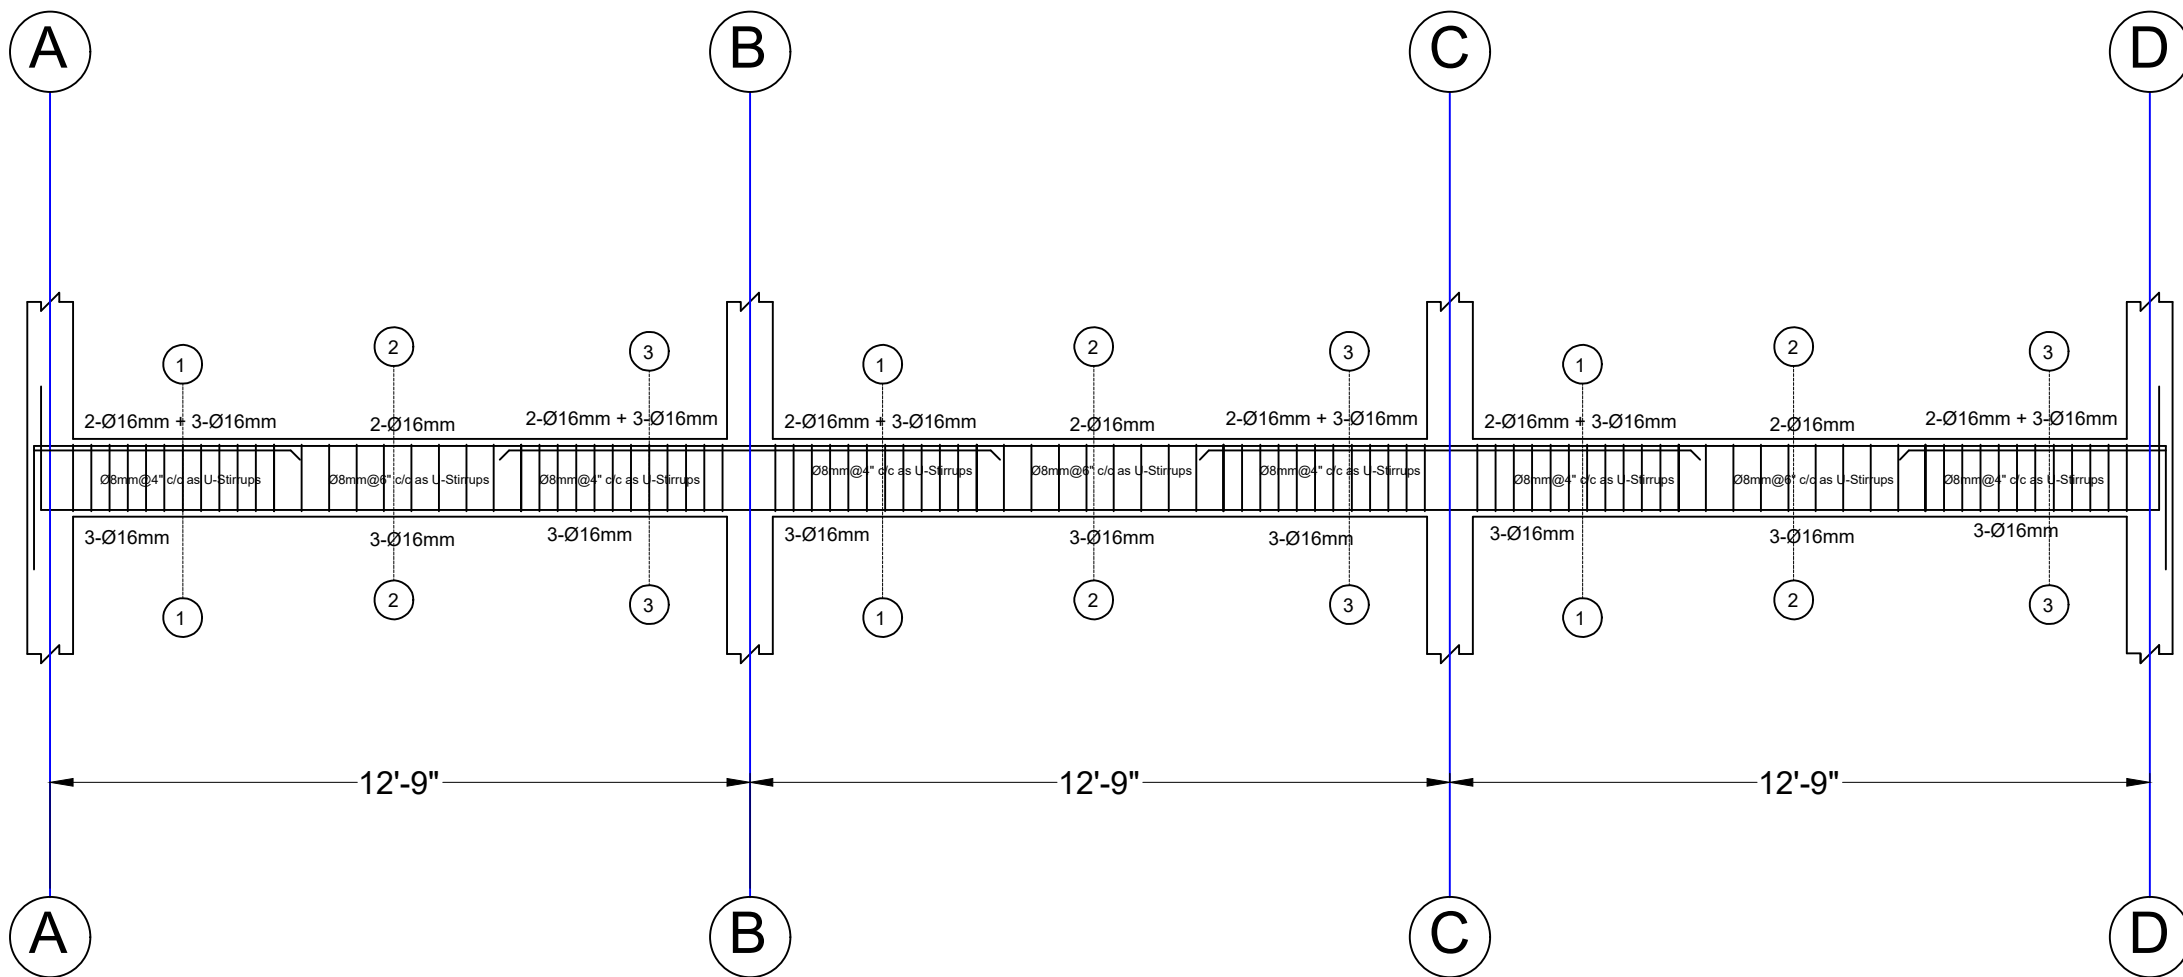

L-Section Detailing of Beam Along 1-1, 2-2, 3-3